


PROPOSED PLAN  
OF  
**MOUNTAIN LAKE PARK**

Scale 200 feet to one inch.

H. E. Paul C.E.

LAND REC: LIBER NO. 6; FOLIO 800  
W. H. T.


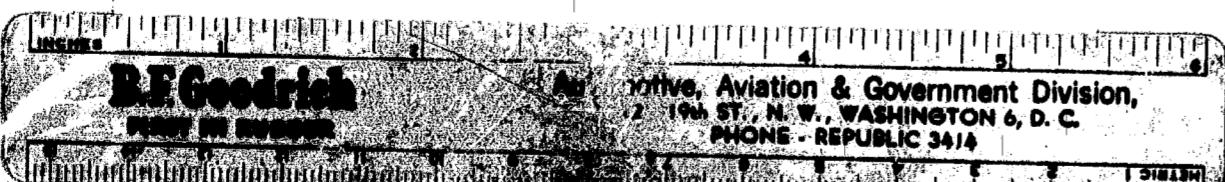


Airline, Aviation & Government Division,  
16th ST., N.W., WASHINGTON 6, D.C.  
PHONE: REPUBLIC 3414




LAND REC: LIBER, NO. 6; FOLIO 800

W. H. T.

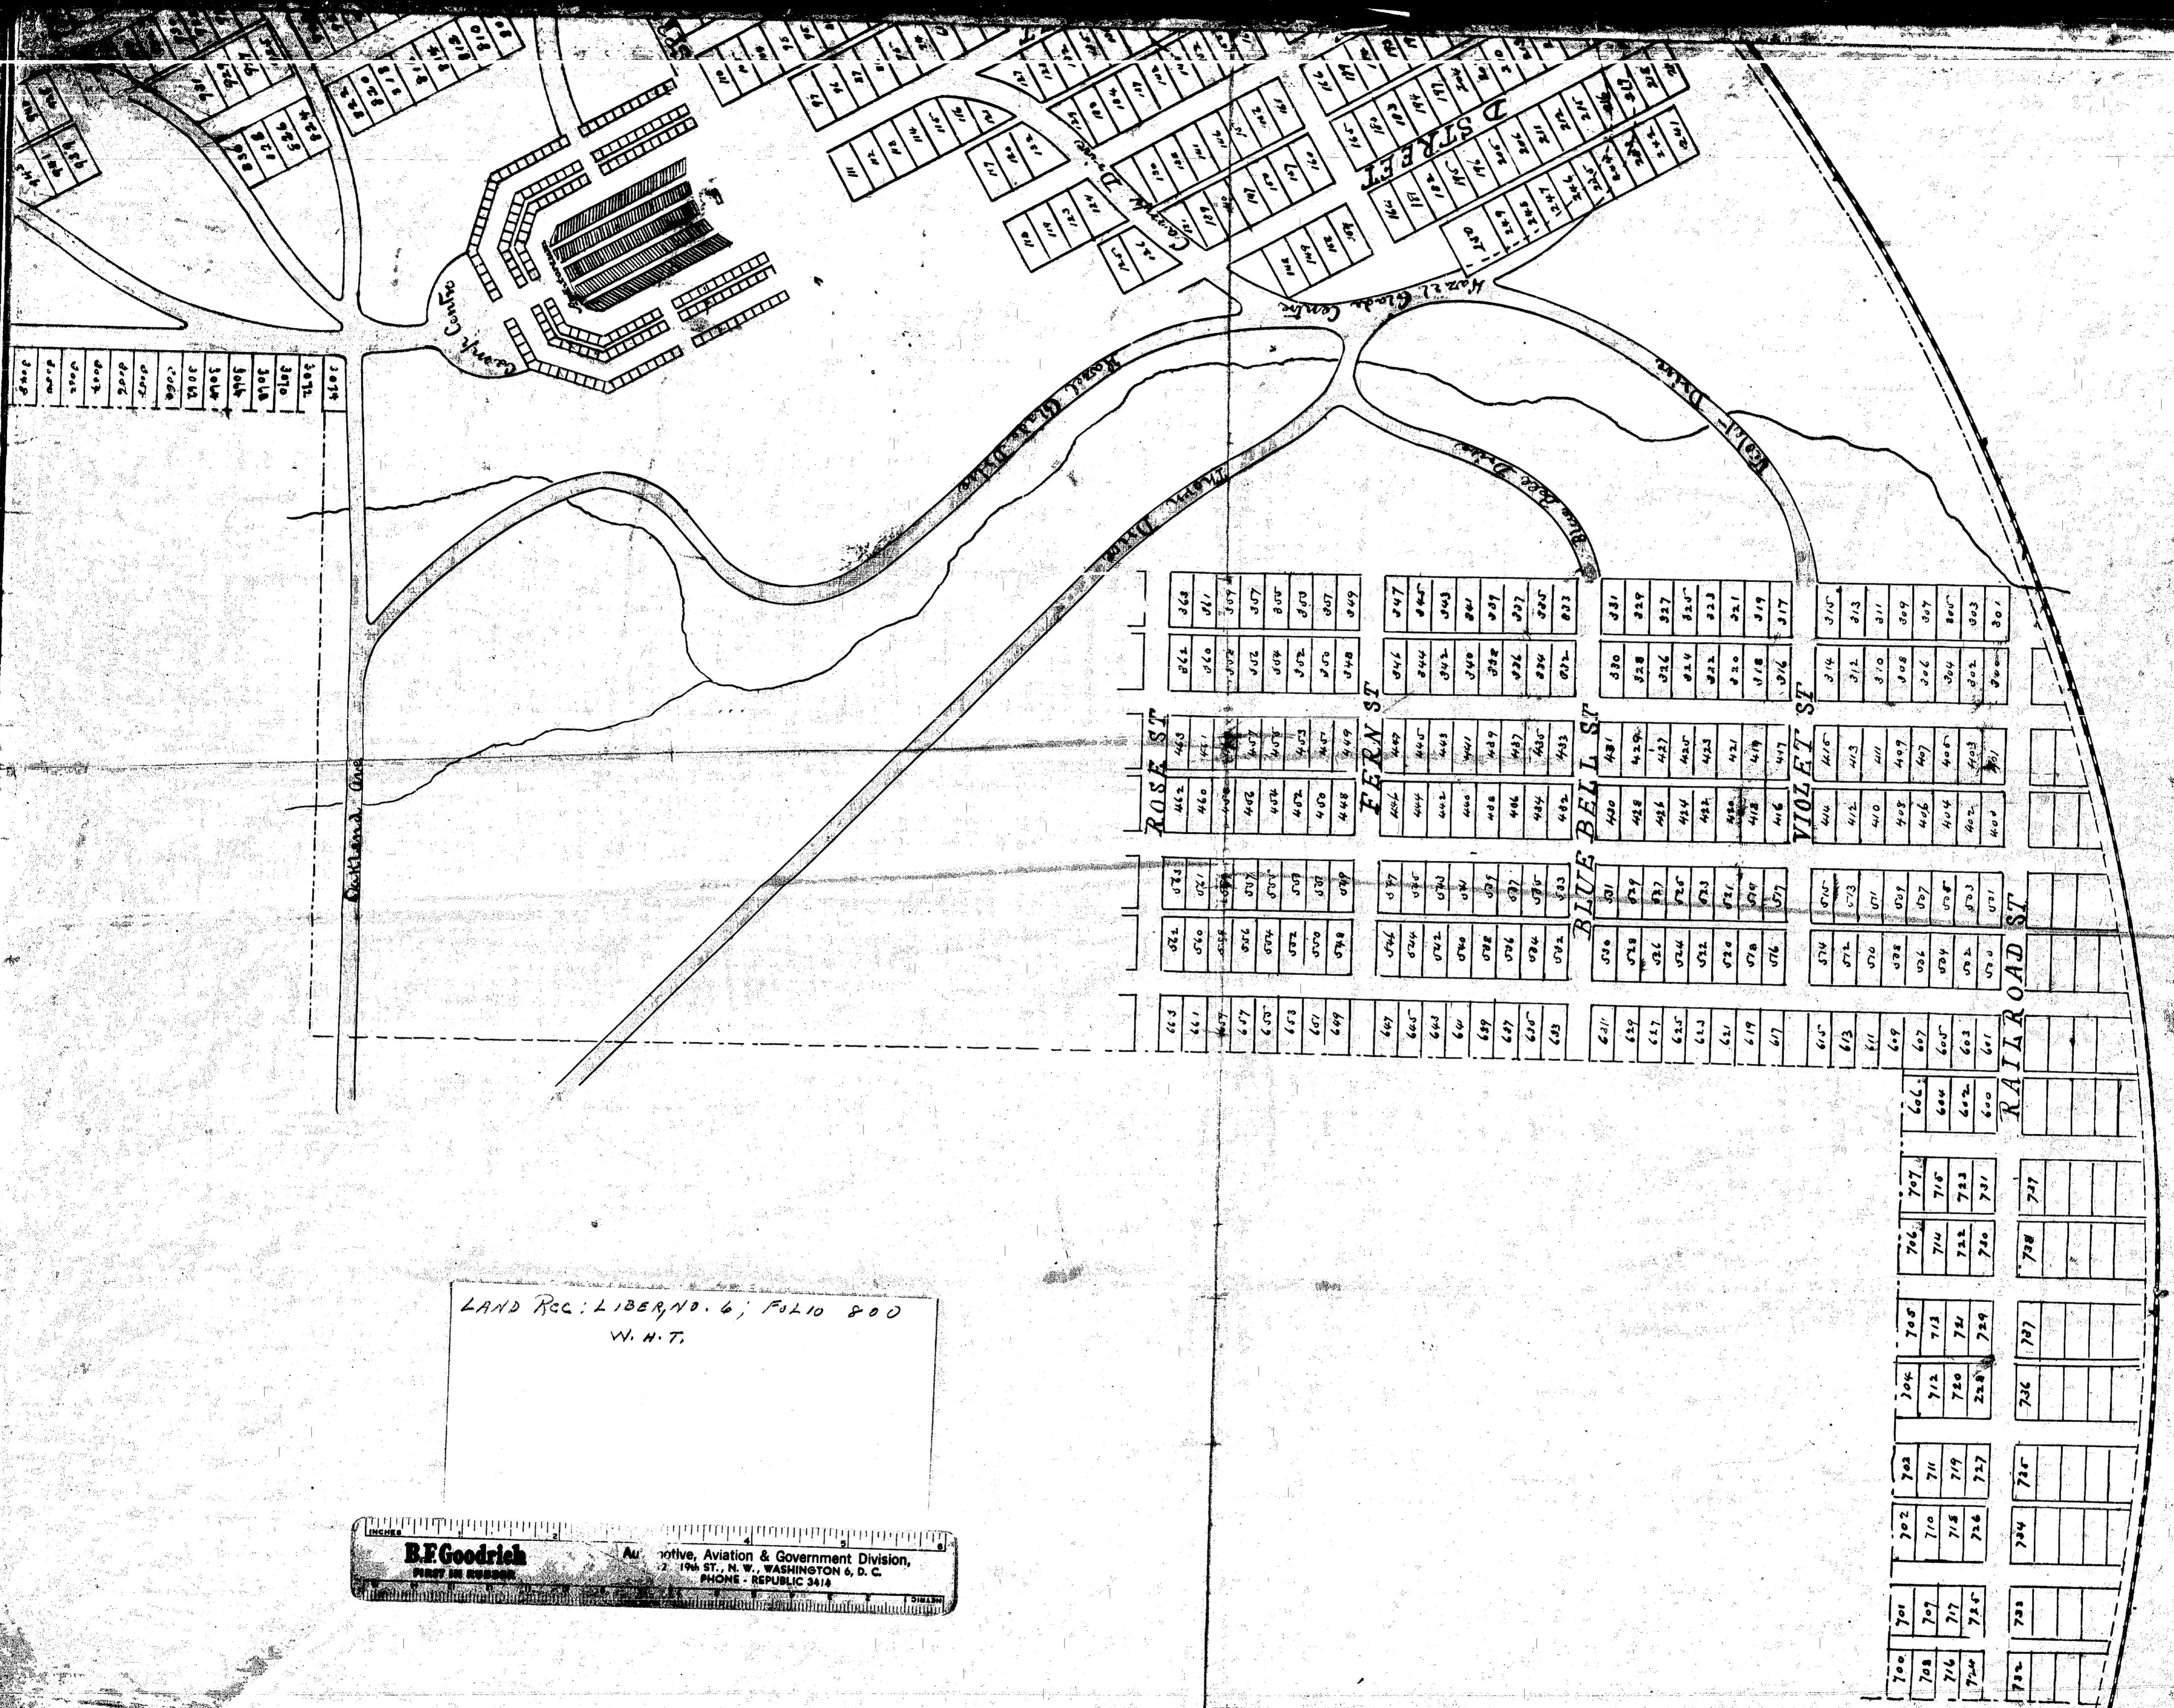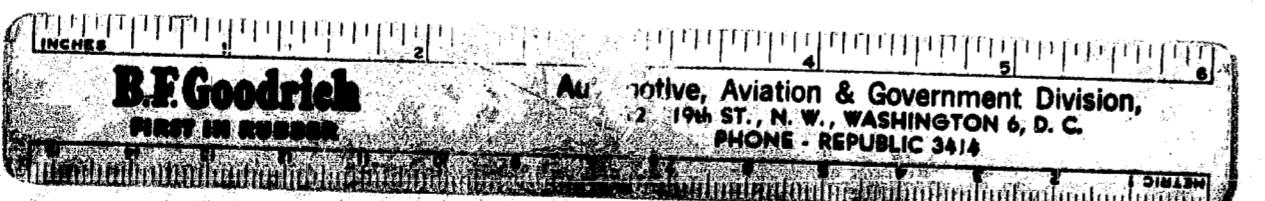

GARRETT COUNTY CIRCUIT COURT (Plats on Microfilm, GA) Land Records WHT 6, p. 800, MSA\_S1539\_11. Date available: Printed 07/15/2019

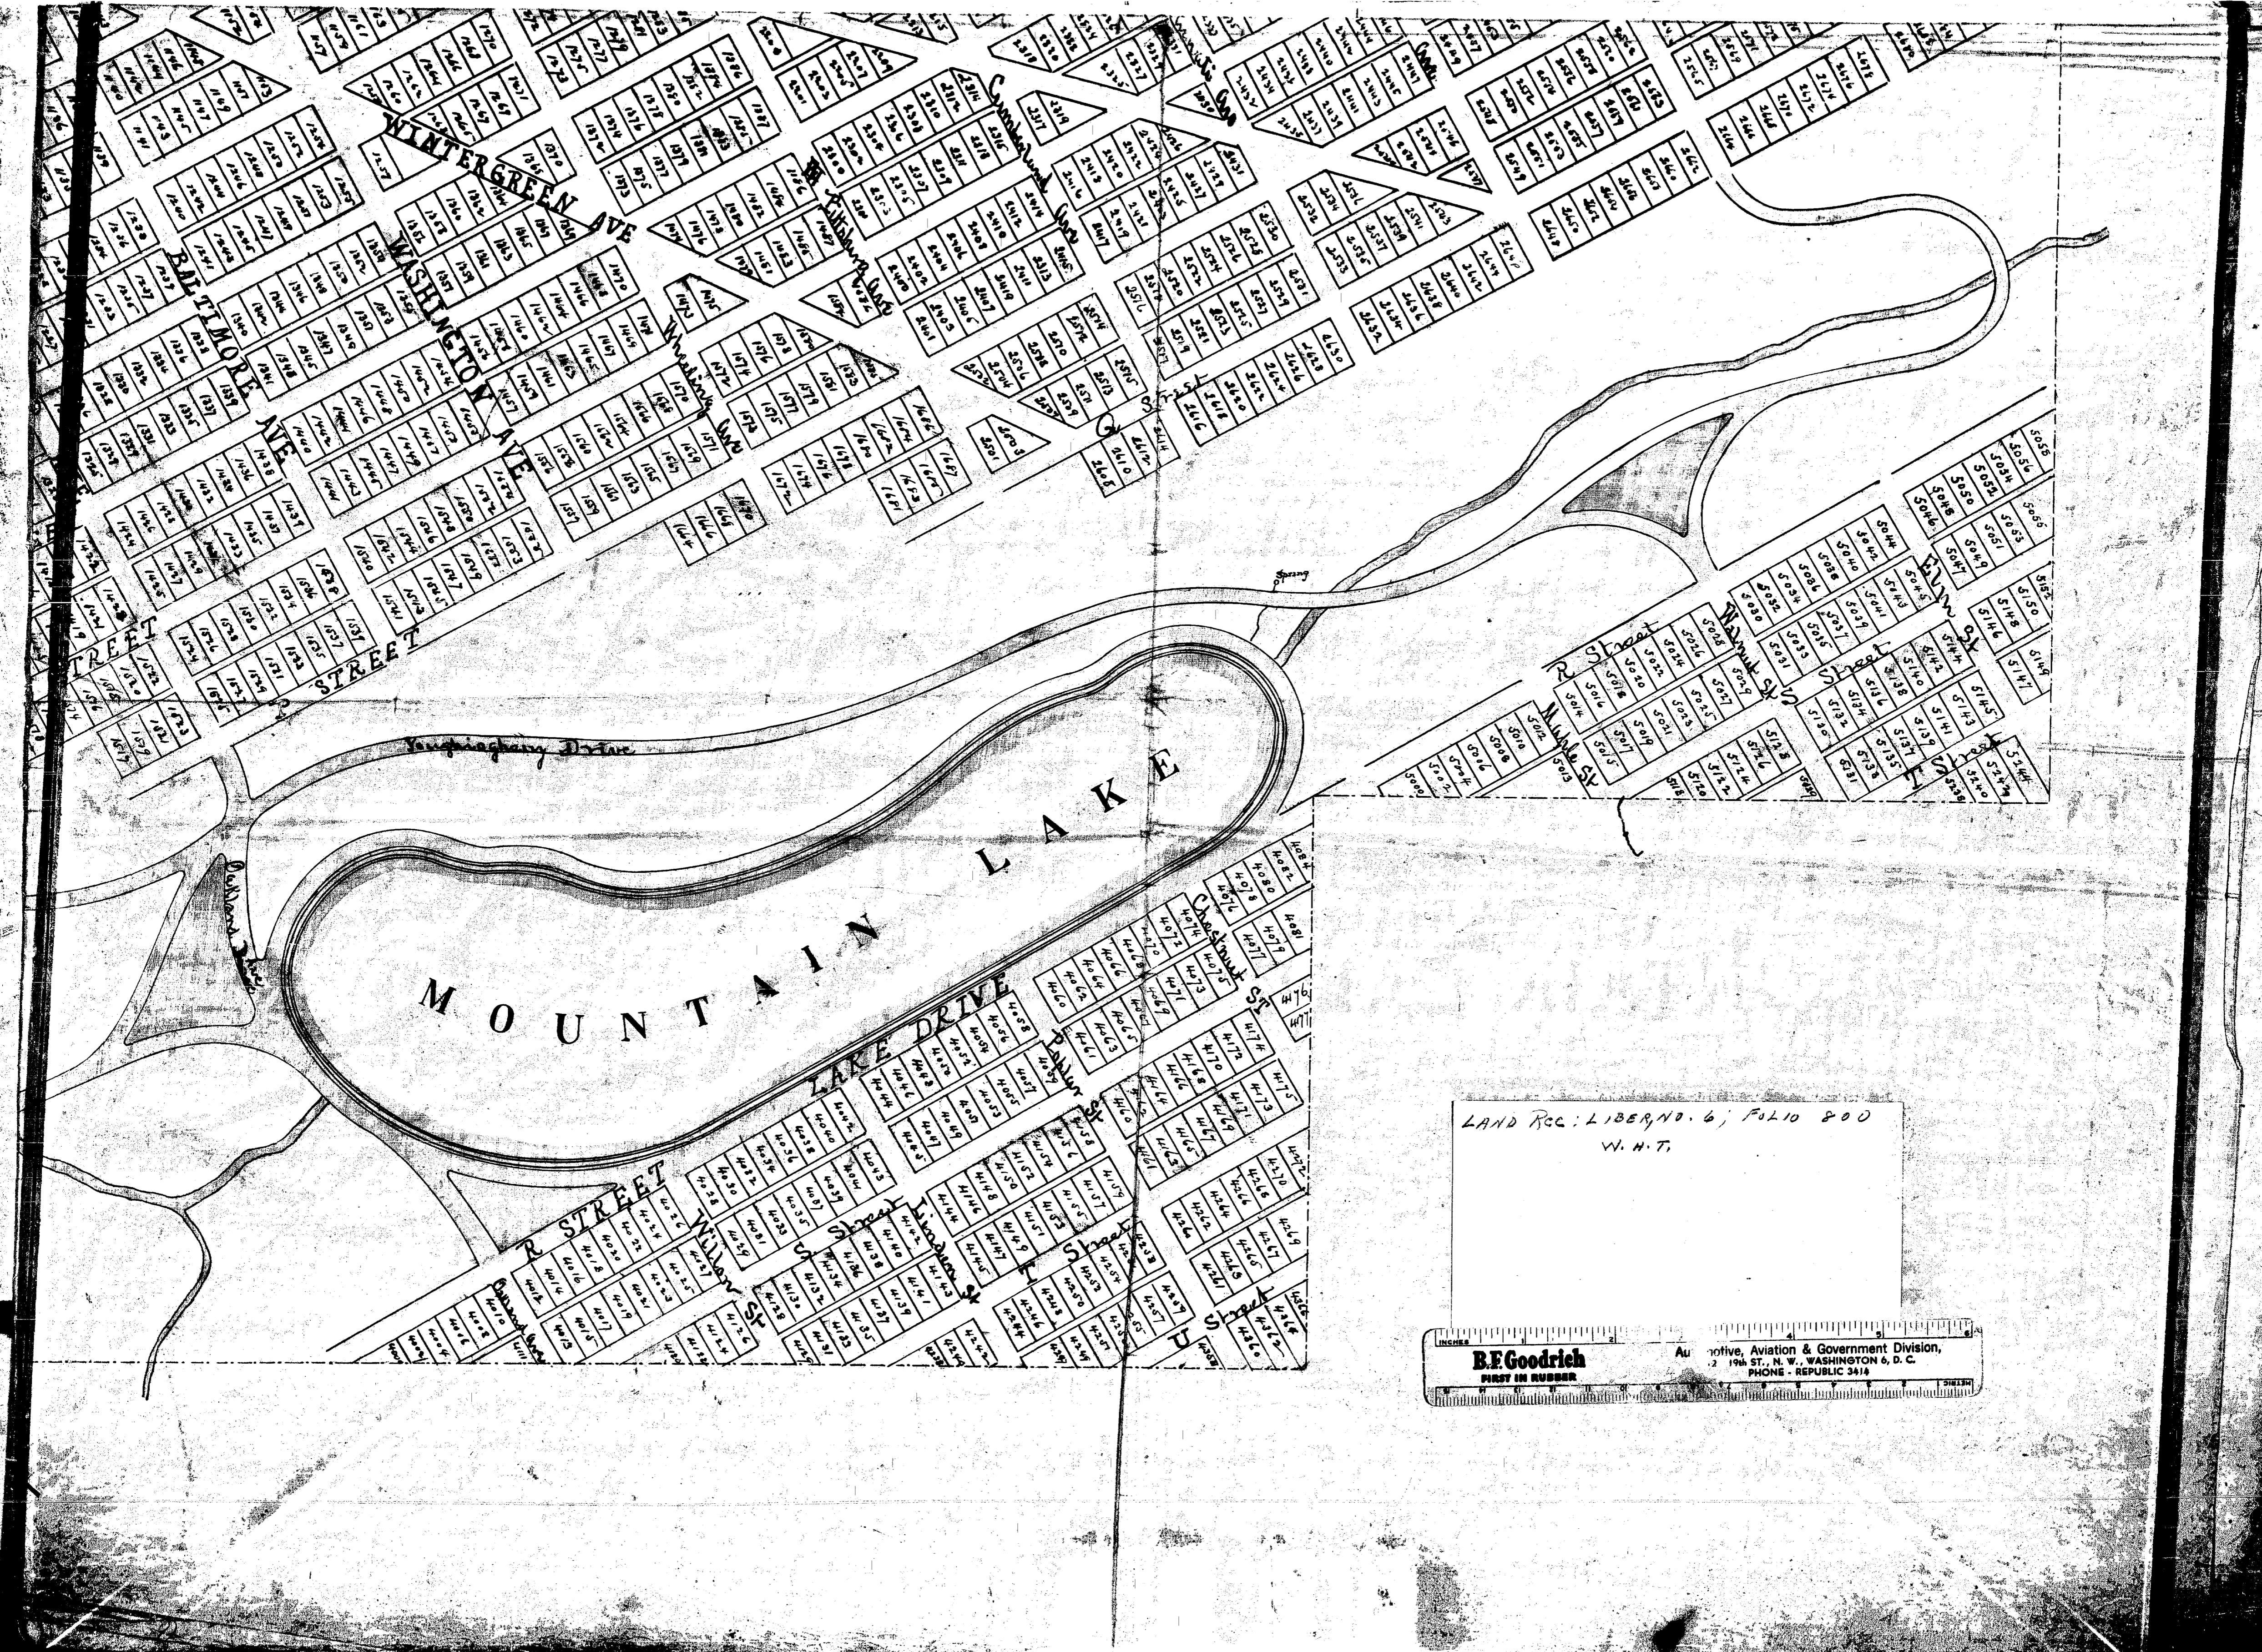



LAND REC: LIBER NO. 6; FOLIO 800  
W. H. T.

